


*** Le coffret SUPP est a déterminer suivant l'intensité de réglage de l'AGCP.**

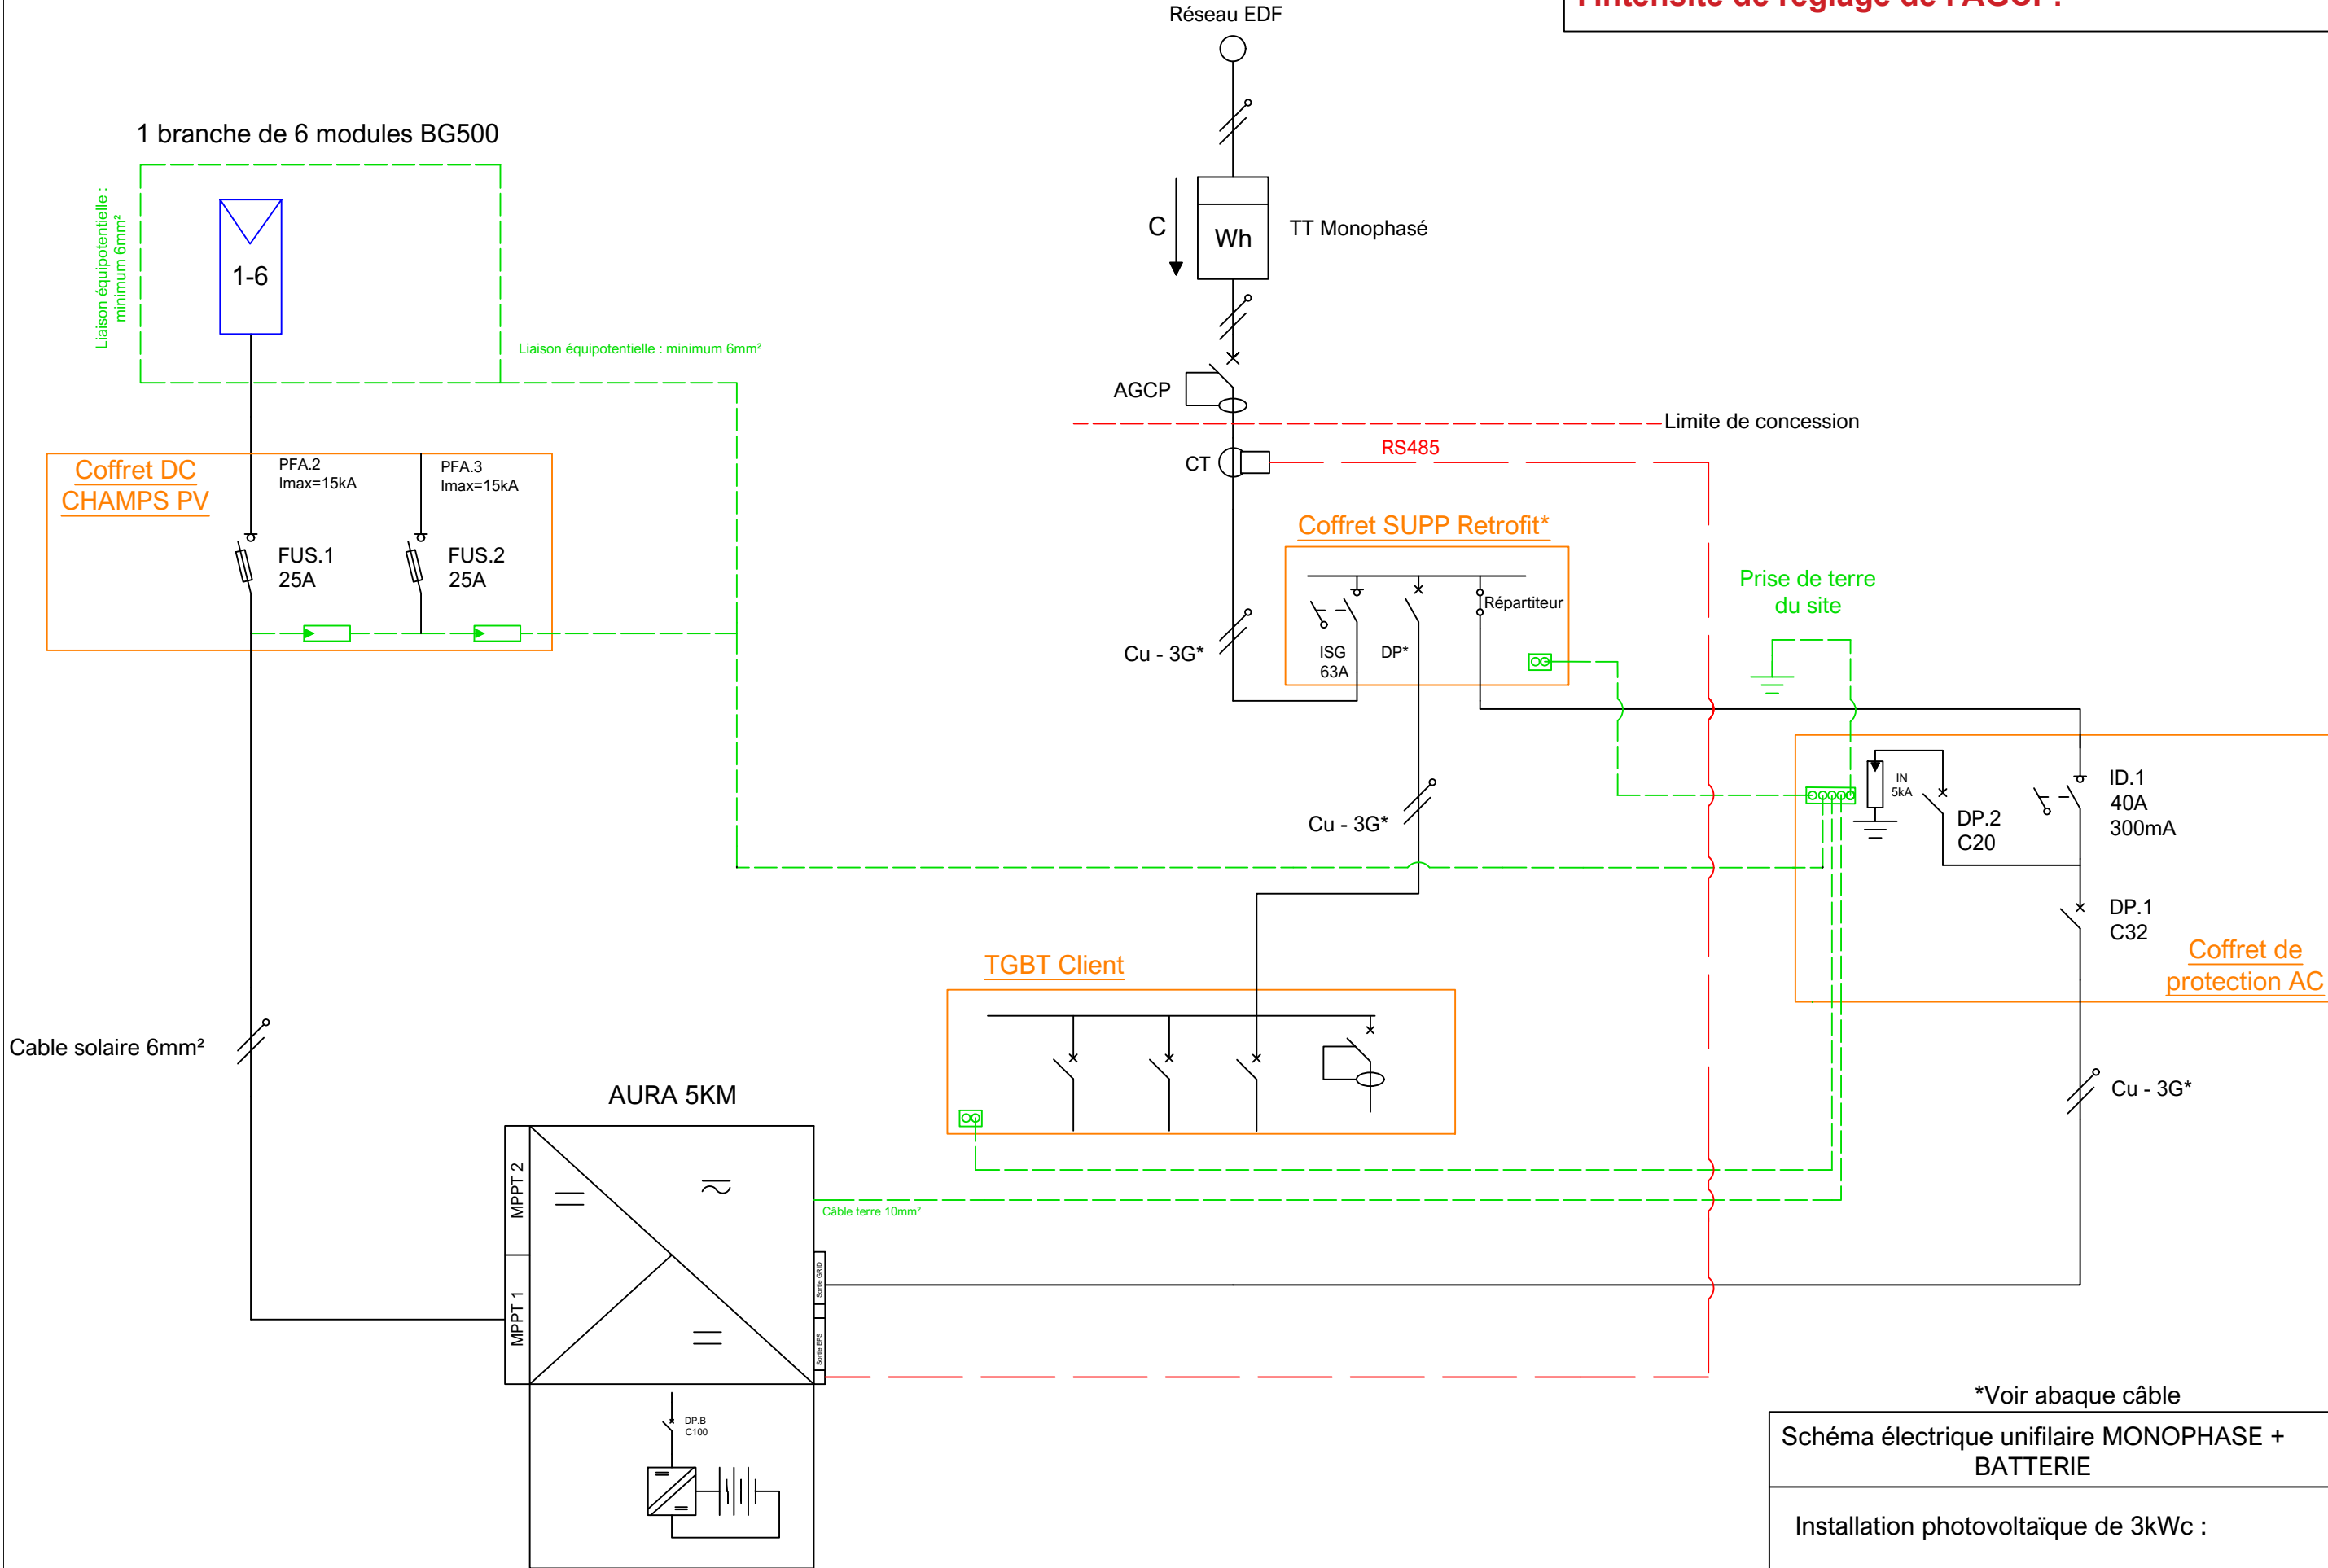

*Voir abaque câble

Schéma électrique unifilaire MONOPHASE + BATTERIE

Installation photovoltaïque de 3kWc :

- 6 modules BG 500Wc
- AURA 5KM-BG