


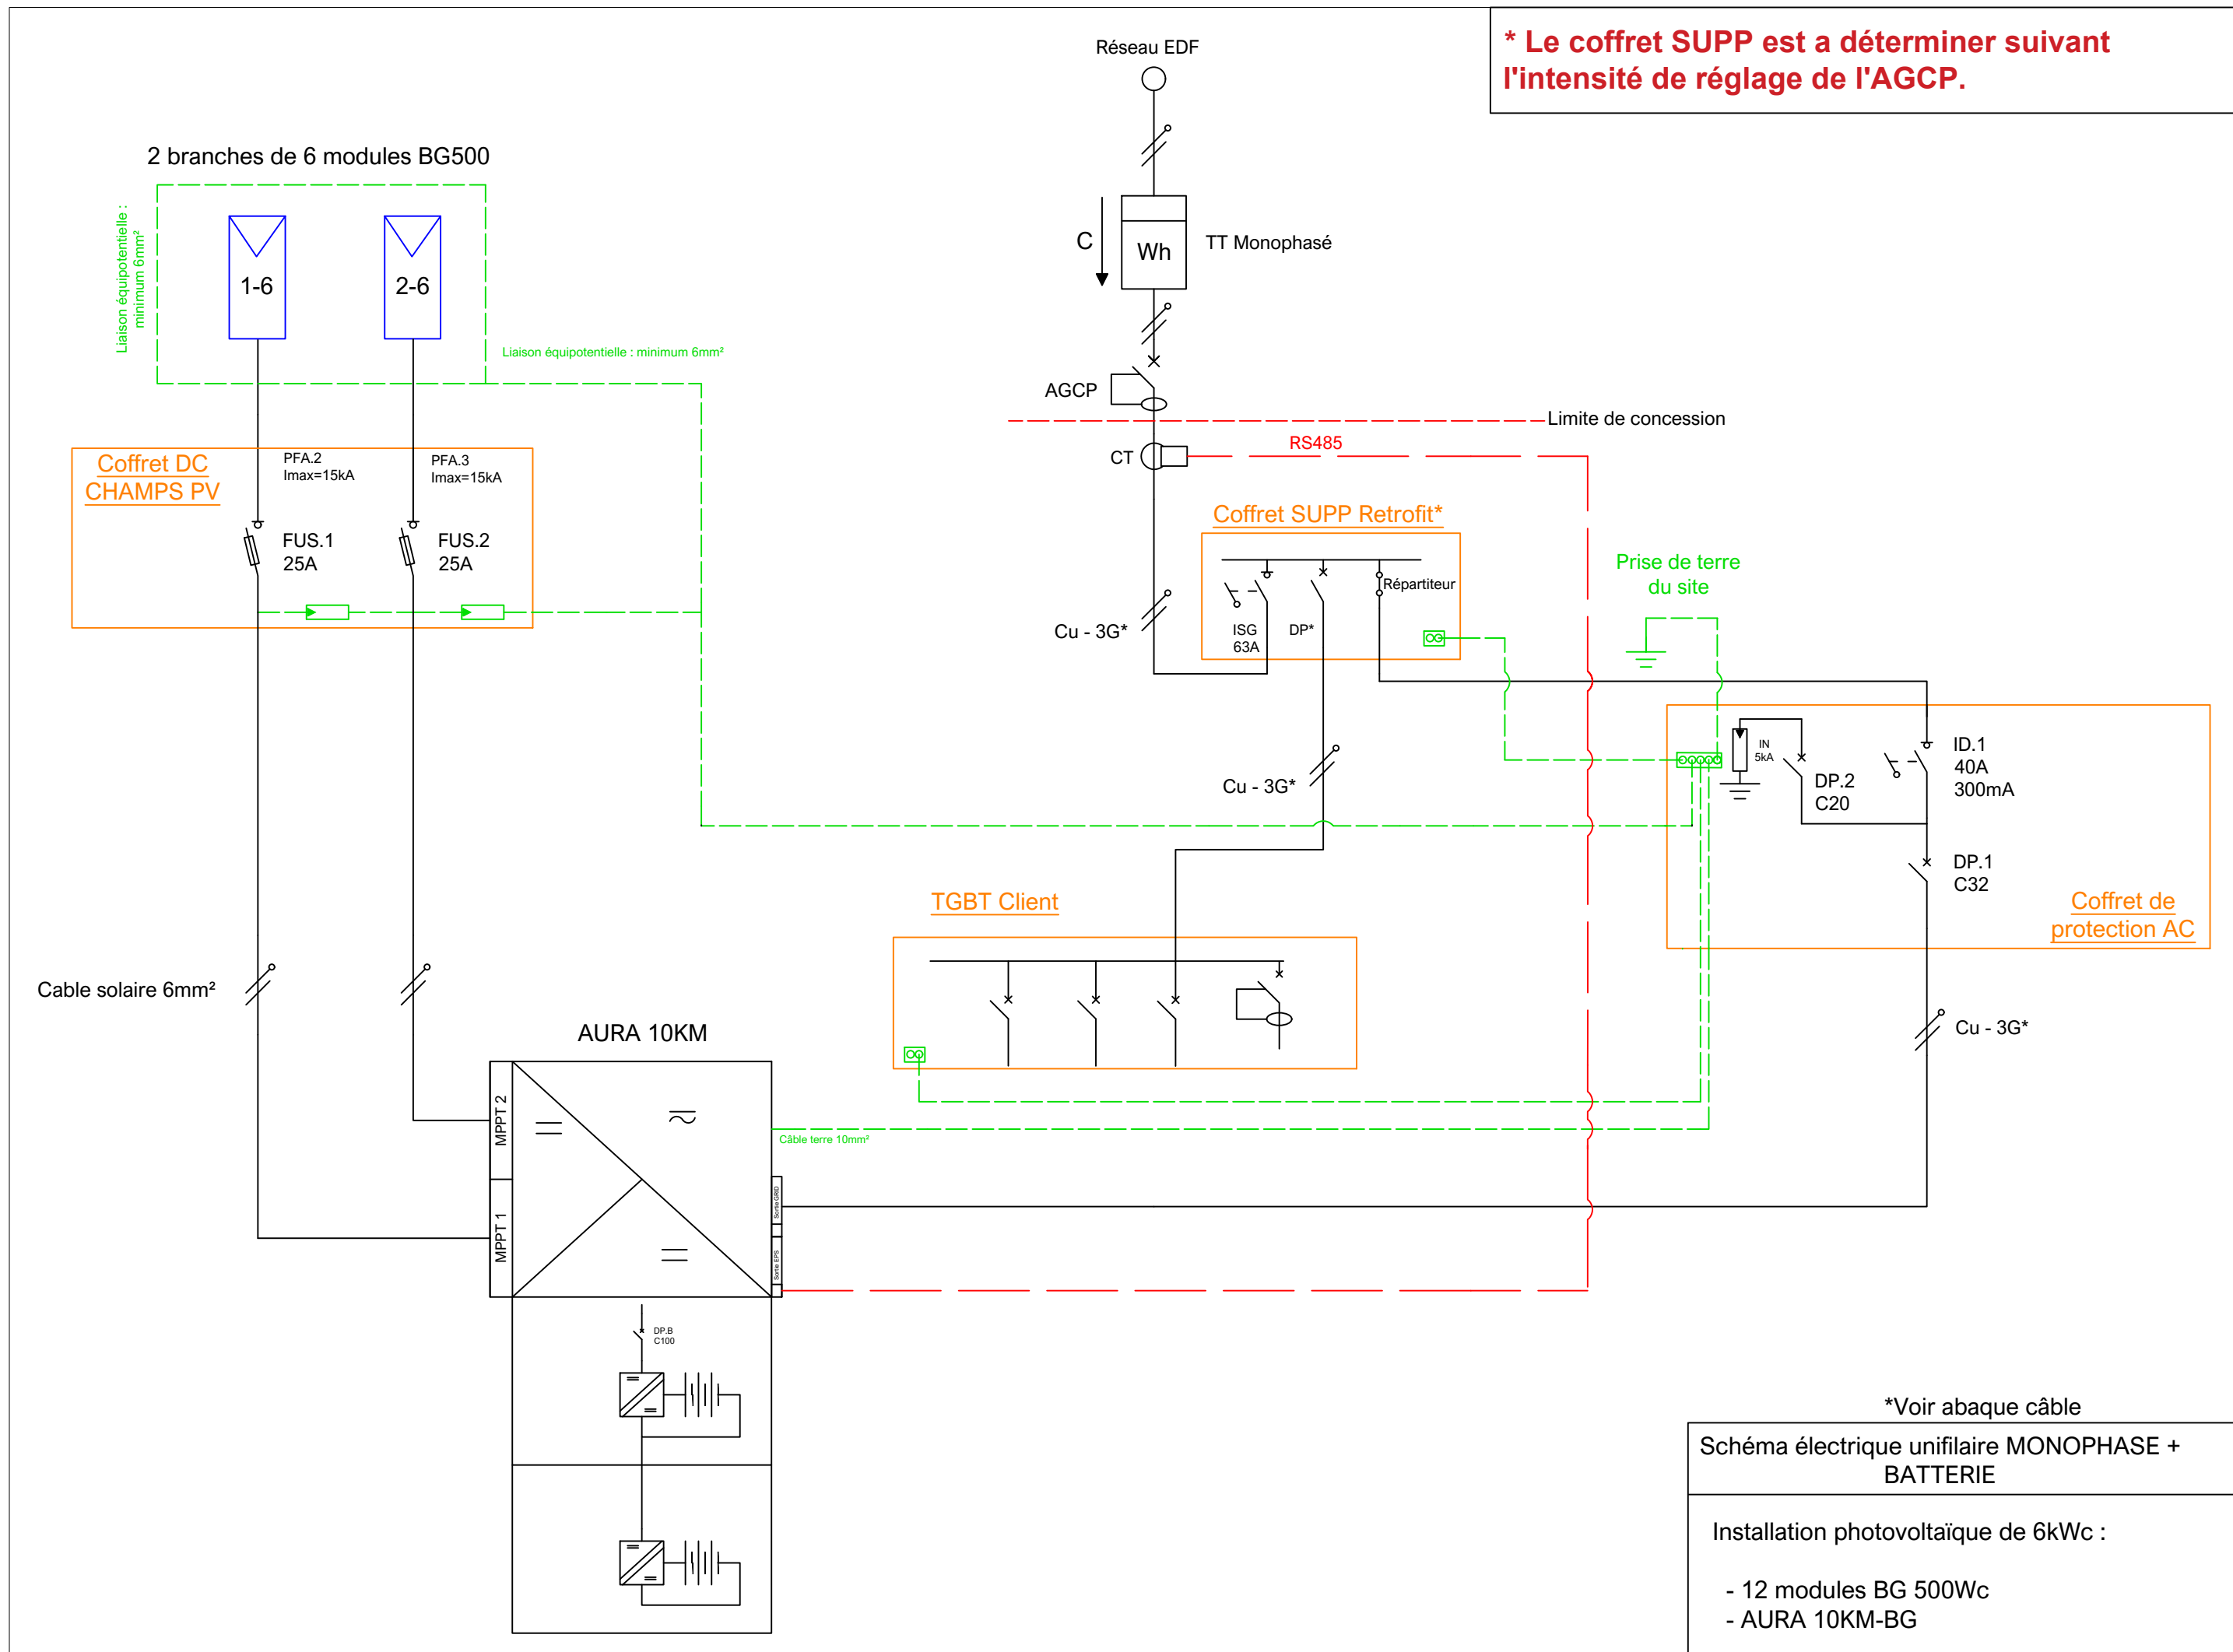

\*Voir abaque câble

Schéma électrique unifilaire MONOPHASE + BATTERIE

Installation photovoltaïque de 6kWc :

- 12 modules BG 500Wc
- AURA 10KM-BG