


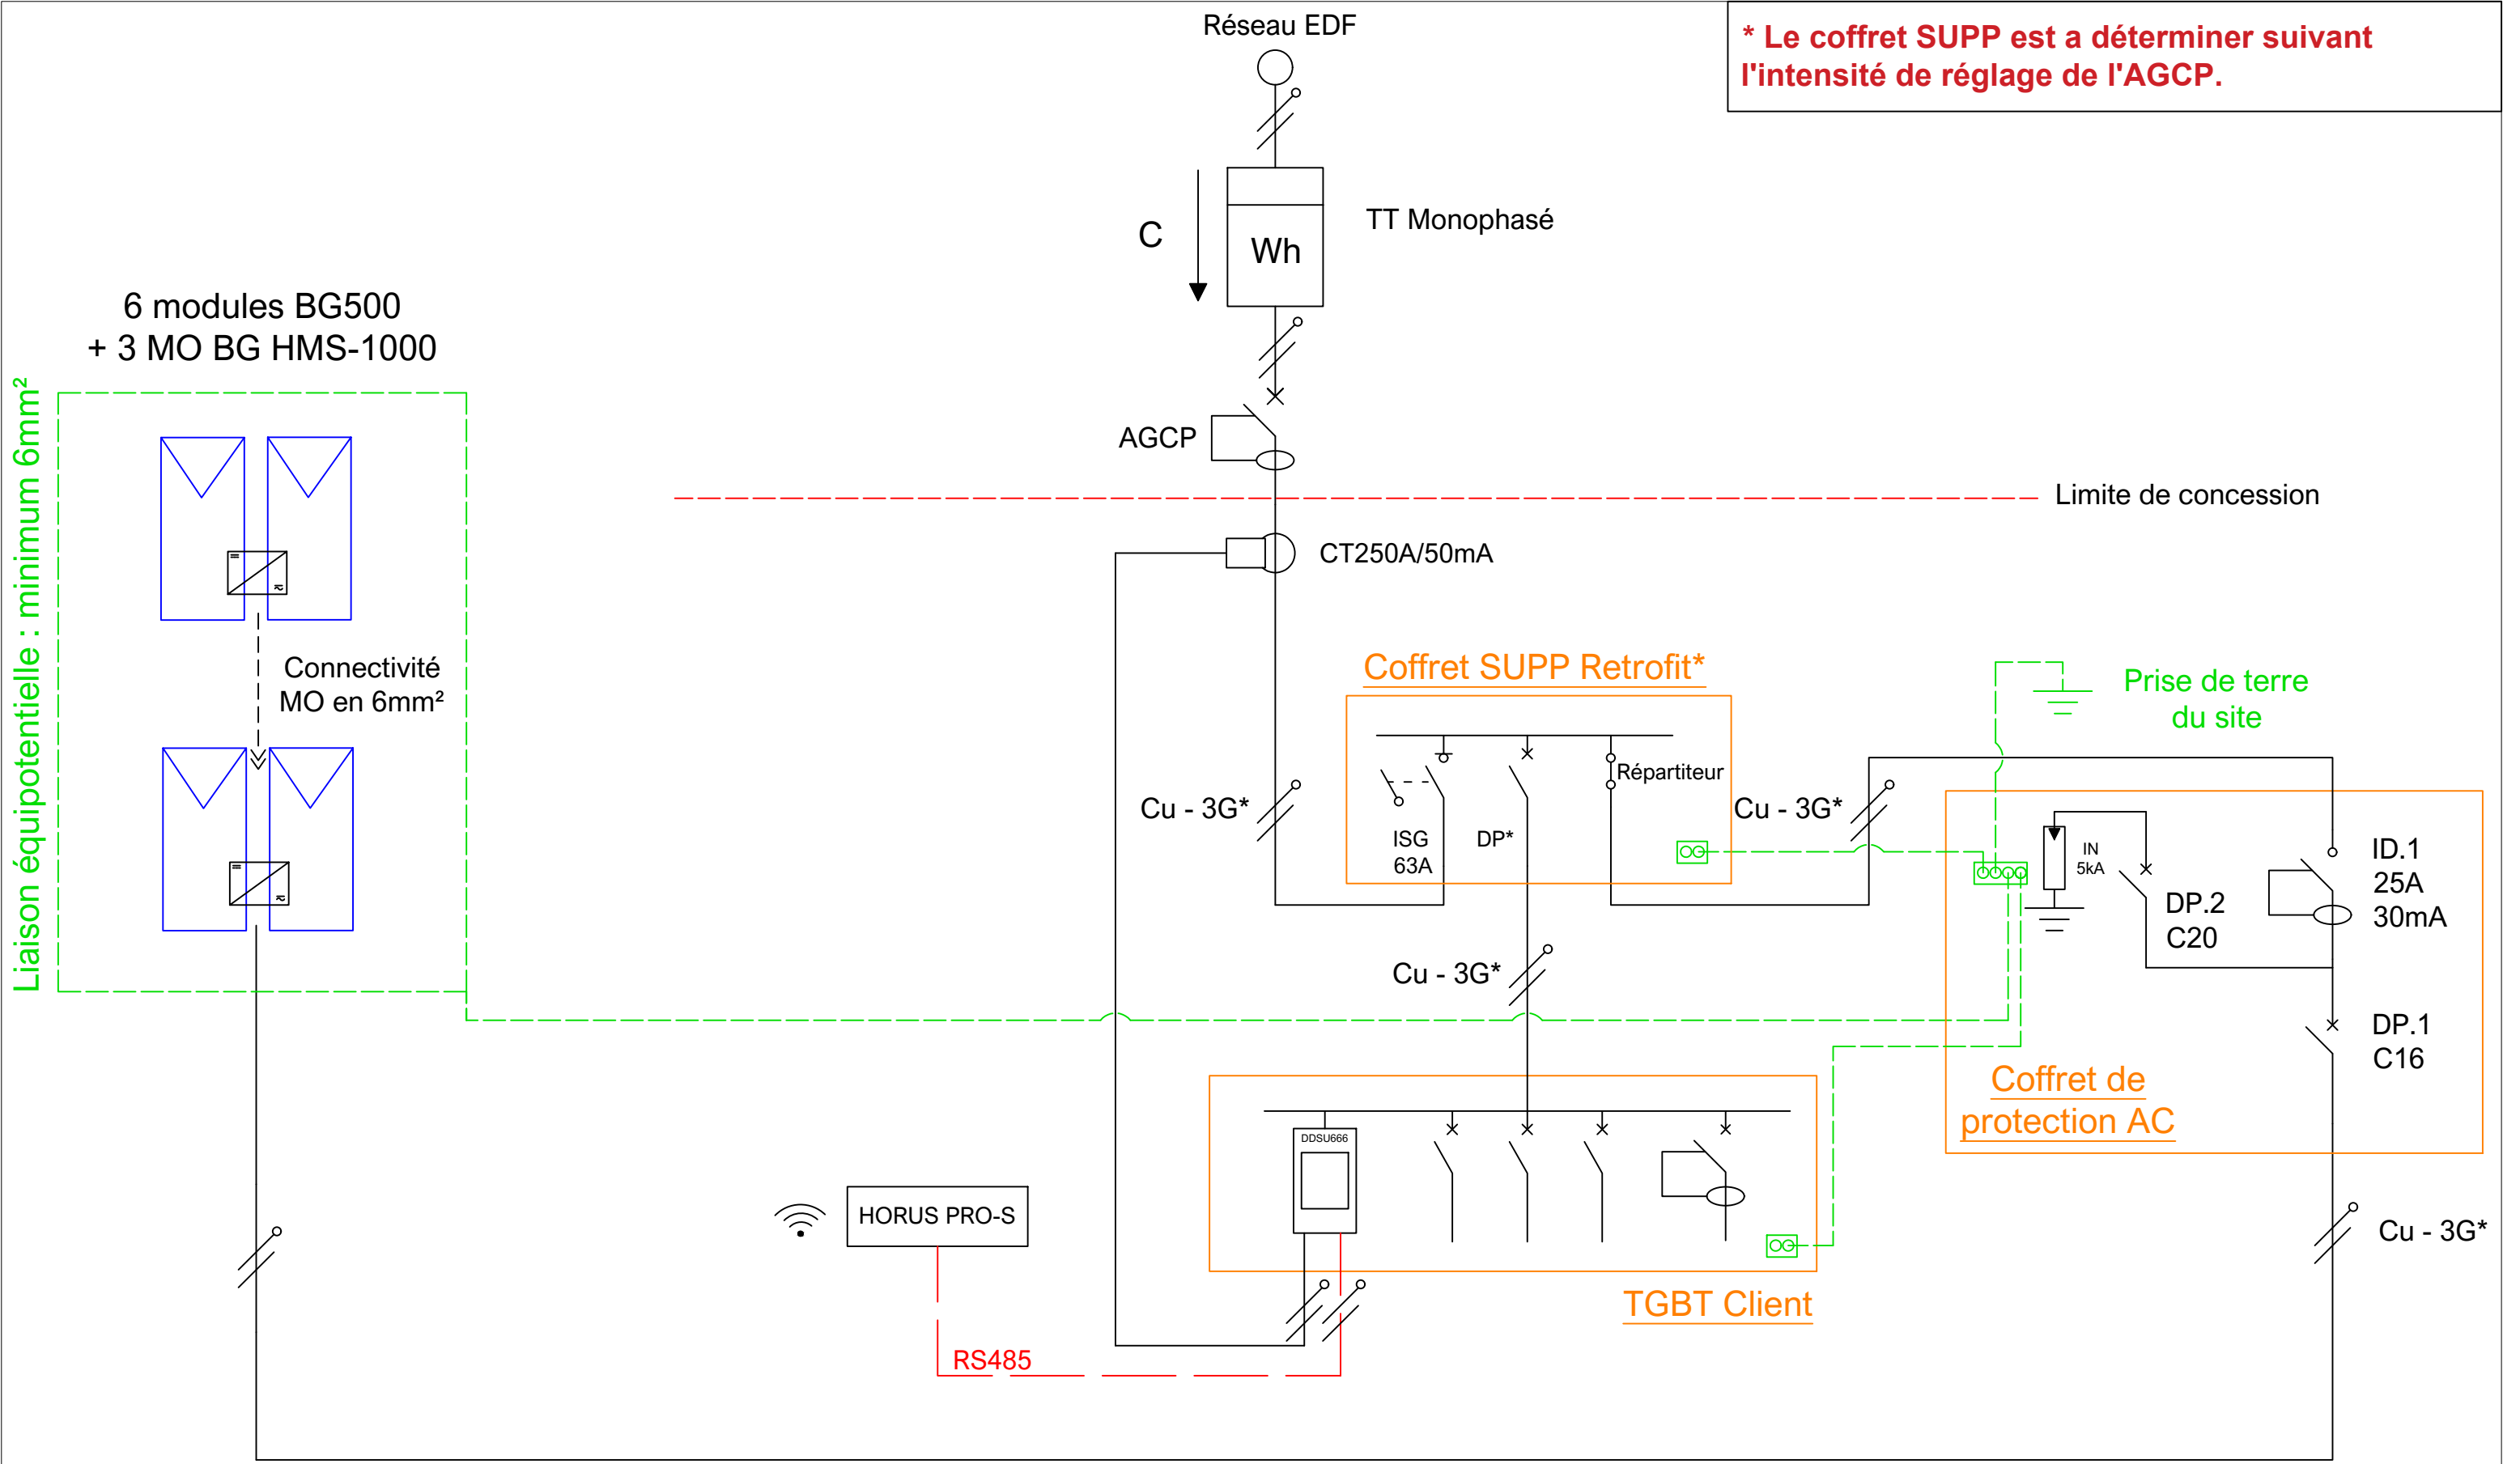

Liaison équipotentielle : minimum 6mm²

* Le coffret SUPP est a déterminer suivant l'intensité de réglage de l'AGCP.

*Voir abaque câble

Schéma électrique unifilaire MONOPHASE
Installation photovoltaïque de 3kWc - 6 modules BG500Wc - 3 Micro Onduleurs BG HMS-1000-2T