


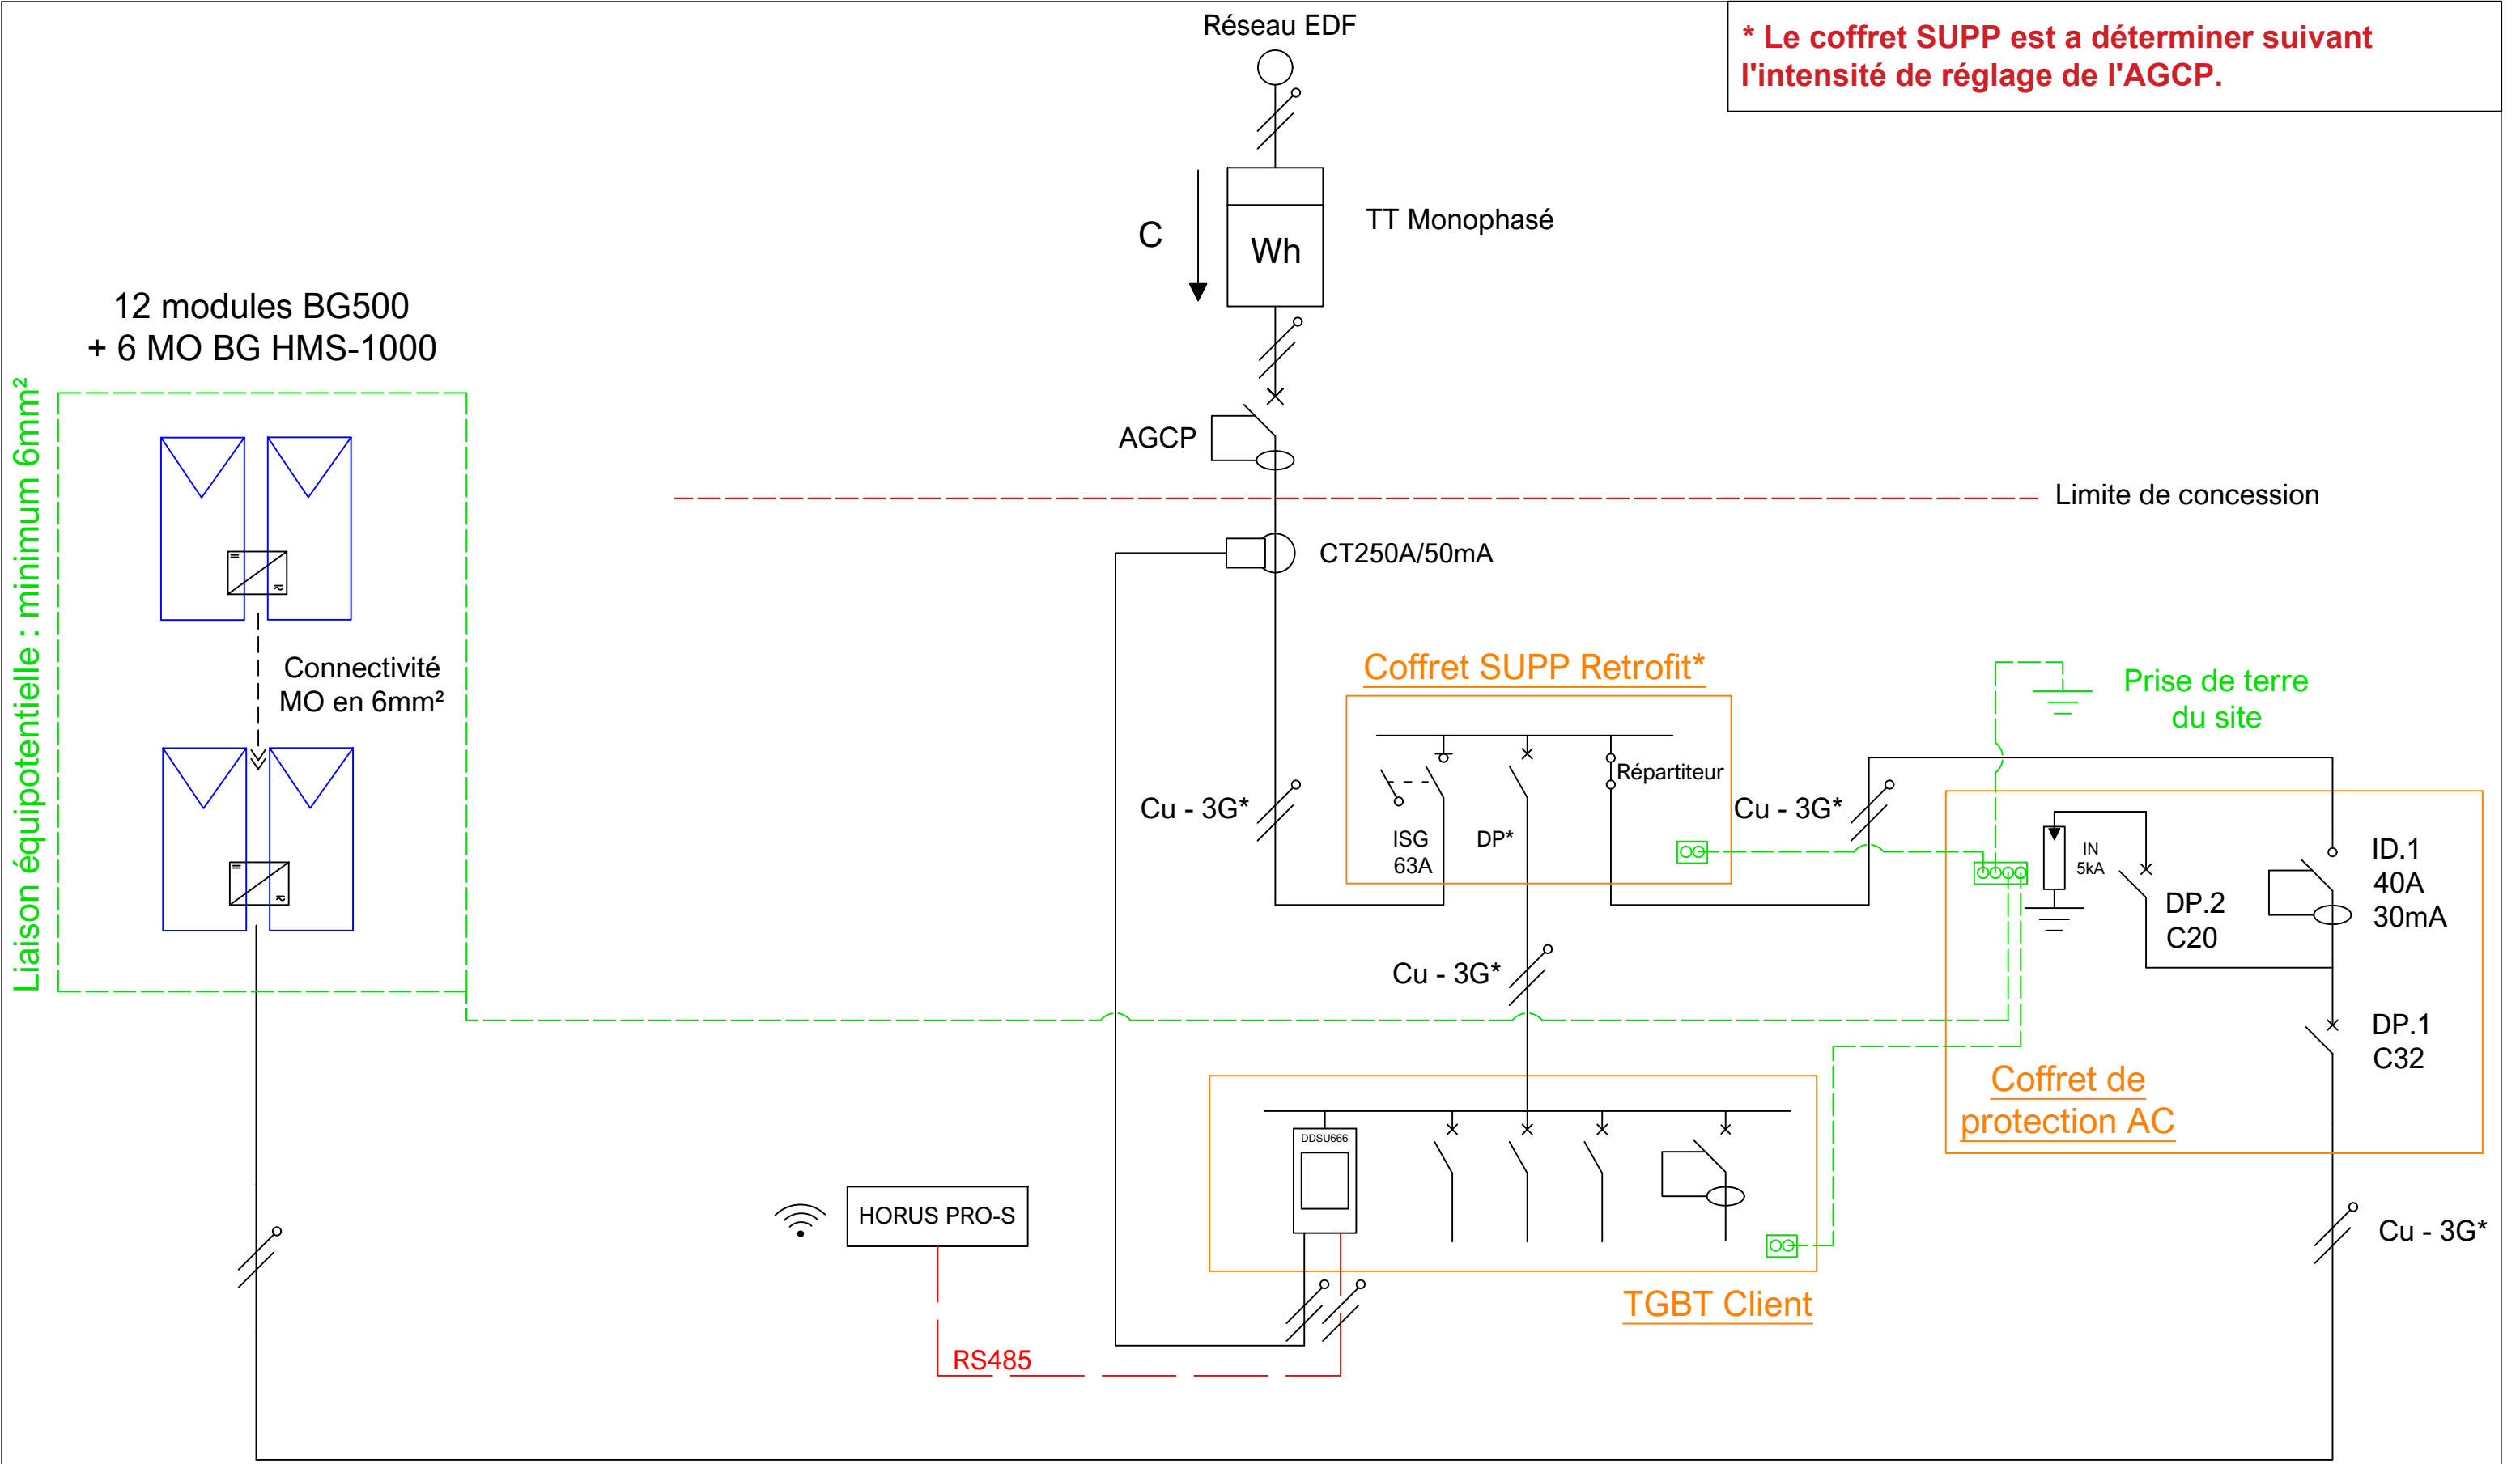

*** Le coffret SUPP est a déterminer suivant l'intensité de réglage de l'AGCP.**

***Voir abaque câble**

Schéma électrique unifilaire MONOPHASE
Installation photovoltaïque de 6kWc - 12 modules BG500Wc - 6 Micro Onduleurs BG HMS-1000-2T